# MEVCUT ABONE

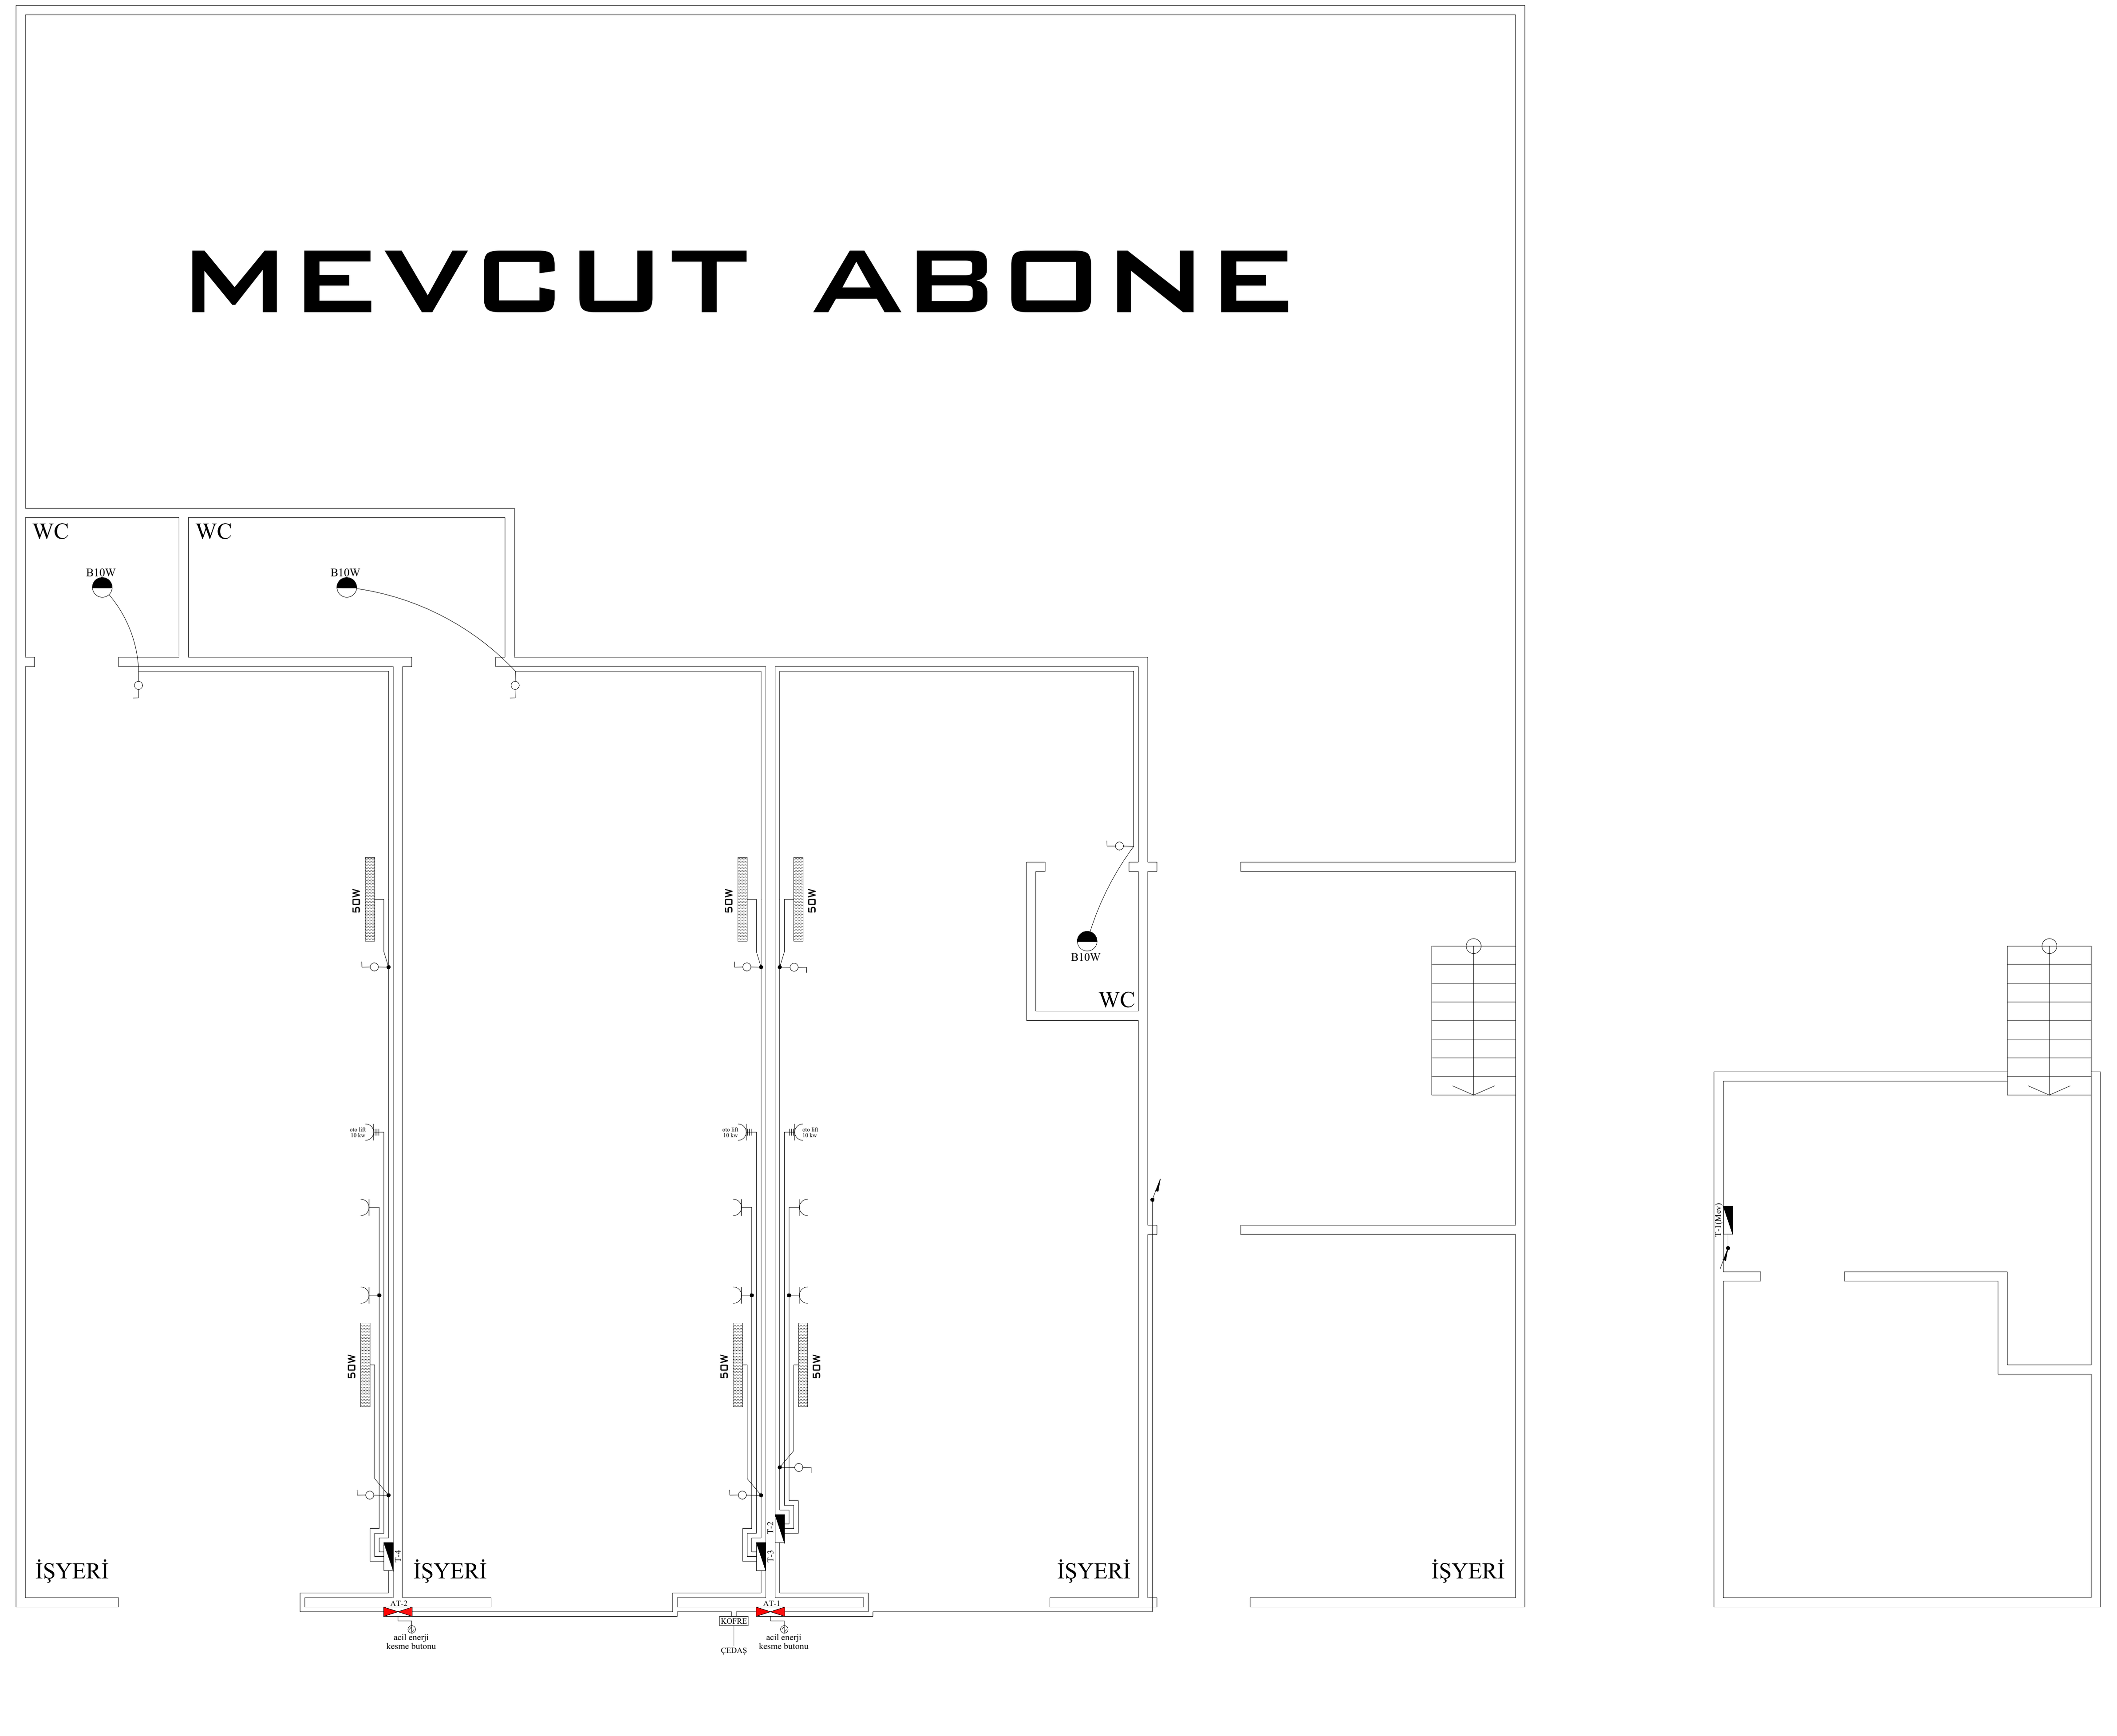


ZEMİN KAT PLANI

1. KAT PLANI

| | KURULU GÜÇ | EŞZAMANLI GÜÇ |
|---|---|---|
| AT-1: | 74.710 W | 74.710 W |
| AT-2: | 21.420 W | 21.420 W |
| TOPLAM | 96.130 W | 96.130 W |

KOFRE = TALEP GÜÇ / 1.73 x U   I = N / 658   I = 96.130 / 658 = 146,09 A

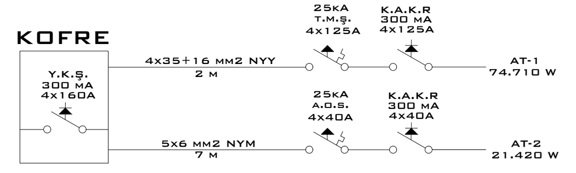


## MEVCUT SAYAÇ SERİ NO: 600108008

## YÜKLEME TABLOSU AT-1

| TOPLAM GÜÇ (W) | TABLO GÜCÜ | TABLO ADI | TABLO CİNSİ | LİNYE NO | IŞIK | PRİZ | LİNYE GÜCÜ | SİGORTA AKIMI | SİGORTA AKIMI | SİGORTA CİNSİ | FAZ | KABLO KESİTİ | AÇIKLAMALAR | EŞ. KATS. | EŞ. GÜÇ (W) |
|---|---|---|---|---|---|---|---|---|---|---|---|---|---|---|---|
| 74.710 | 64.000 | T-1 | Ş.P. | MEVCUT ABONE | | | | | | | | | | 100% | 64.000 |
| | 10.710 | T-2 | Ş.P. | 1 | | 2 | 600 | B16 | 3 kA | WOTO | R | 3x2,5 mm² NYA | PRİZ | 100% | 10.710 |
| | | | | 2 | | 1 | 10.000 | B3x25 | 4,5 kA | WOTO | RST | 5x4 mm² NYM | LİFT | | |
| | | | | 3 | 3 | | 110 | B10 | 3 kA | WOTO | S | 3x2,5 mm² NYA | AYDINLATMA | | |

## ISINMA KONTROLÜ HESABI

ANA KOLON = TALEP GÜÇ / 1.73xU   I = N/658   I = 74.710 / 658 = 113,54 A

I = N / 658 = 74.710 / 658 = 113,54 A < 129 OLD. 4x35+16 NYY KULLANILMASI UYGUNDUR.

## GERİLİM DÜŞÜMÜ HESABI T-1

I = N / 658 = 10.710 / 658 = 16,27 A < 43 OLD. 5x6 NYM KULLANILMASI UYGUNDUR.

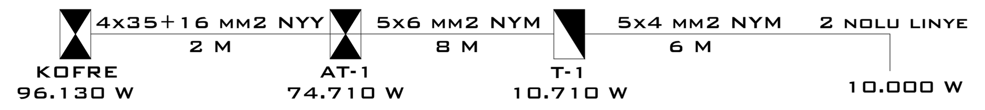


%E = 0,0000124x(LxN/S) + 0,0000124x(LxN/S) + 0,0000124x(LxN/S) =

%E = 0,0000124x(2x74.710/35) + 0,0000124x(8x10.710/6) + 0,0000124x(6x10.000/4) =

%E = 0,05 + 0,17 + 0,18 = 0,40 V < 1,5 V

## YÜKLEME TABLOSU AT-2

| TOPLAM GÜÇ (W) | TABLO GÜCÜ | TABLO ADI | TABLO CİNSİ | LİNYE NO | IŞIK | PRİZ | LİNYE GÜCÜ | SİGORTA AKIMI | SİGORTA AKIMI | SİGORTA CİNSİ | FAZ | KABLO KESİTİ | AÇIKLAMALAR | EŞ. KATS. | EŞ. GÜÇ (W) |
|---|---|---|---|---|---|---|---|---|---|---|---|---|---|---|---|
| 21.420 | 10.710 | T-3 | Ş.P. | 1 | | 2 | 600 | B16 | 3 kA | WOTO | R | 3x2,5 mm² NYA | PRİZ | 100% | 10.710 |
| | | | | 2 | | 1 | 10.000 | B3x25 | 4,5 kA | WOTO | RST | 5x4 mm² NYM | LİFT | | |
| | | | | 3 | 3 | | 110 | B10 | 3 kA | WOTO | S | 3x2,5 mm² NYA | AYDINLATMA | | |
| | 10.710 | T-4 | Ş.P. | 1 | | 2 | 600 | B16 | 3 kA | WOTO | R | 3x2,5 mm² NYA | PRİZ | 100% | 10.710 |
| | | | | 2 | | 1 | 10.000 | B3x25 | 4,5 kA | WOTO | RST | 5x4 mm² NYM | LİFT | | |
| | | | | 3 | 3 | | 110 | B10 | 3 kA | WOTO | S | 3x2,5 mm² NYA | AYDINLATMA | | |

## ISINMA KONTROLÜ HESABI

ANA KOLON = TALEP GÜÇ / 1.73xU   I = N/658   I = 21.420 / 658 = 32,55 A

I = N / 658 = 21.420 / 658 = 32,55 A < 43 OLD. 5x6 NYM KULLANILMASI UYGUNDUR.

## GERİLİM DÜŞÜMÜ HESABI T-3

I = N / 658 = 10.710 / 658 = 16,27 A < 43 OLD. 5x6 NYM KULLANILMASI UYGUNDUR.

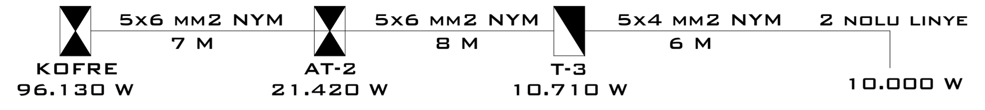


%E = 0,0000124x(LxN/S) + 0,0000124x(LxN/S) + 0,0000124x(LxN/S) =

%E = 0,0000124x(7x21.420/6) + 0,0000124x(8x10.710/6) + 0,0000124x(6x10.000/4) =

%E = 0,31 + 0,17 + 0,18 = 0,66 V < 1,5 V

## KOLON ŞEMALARI

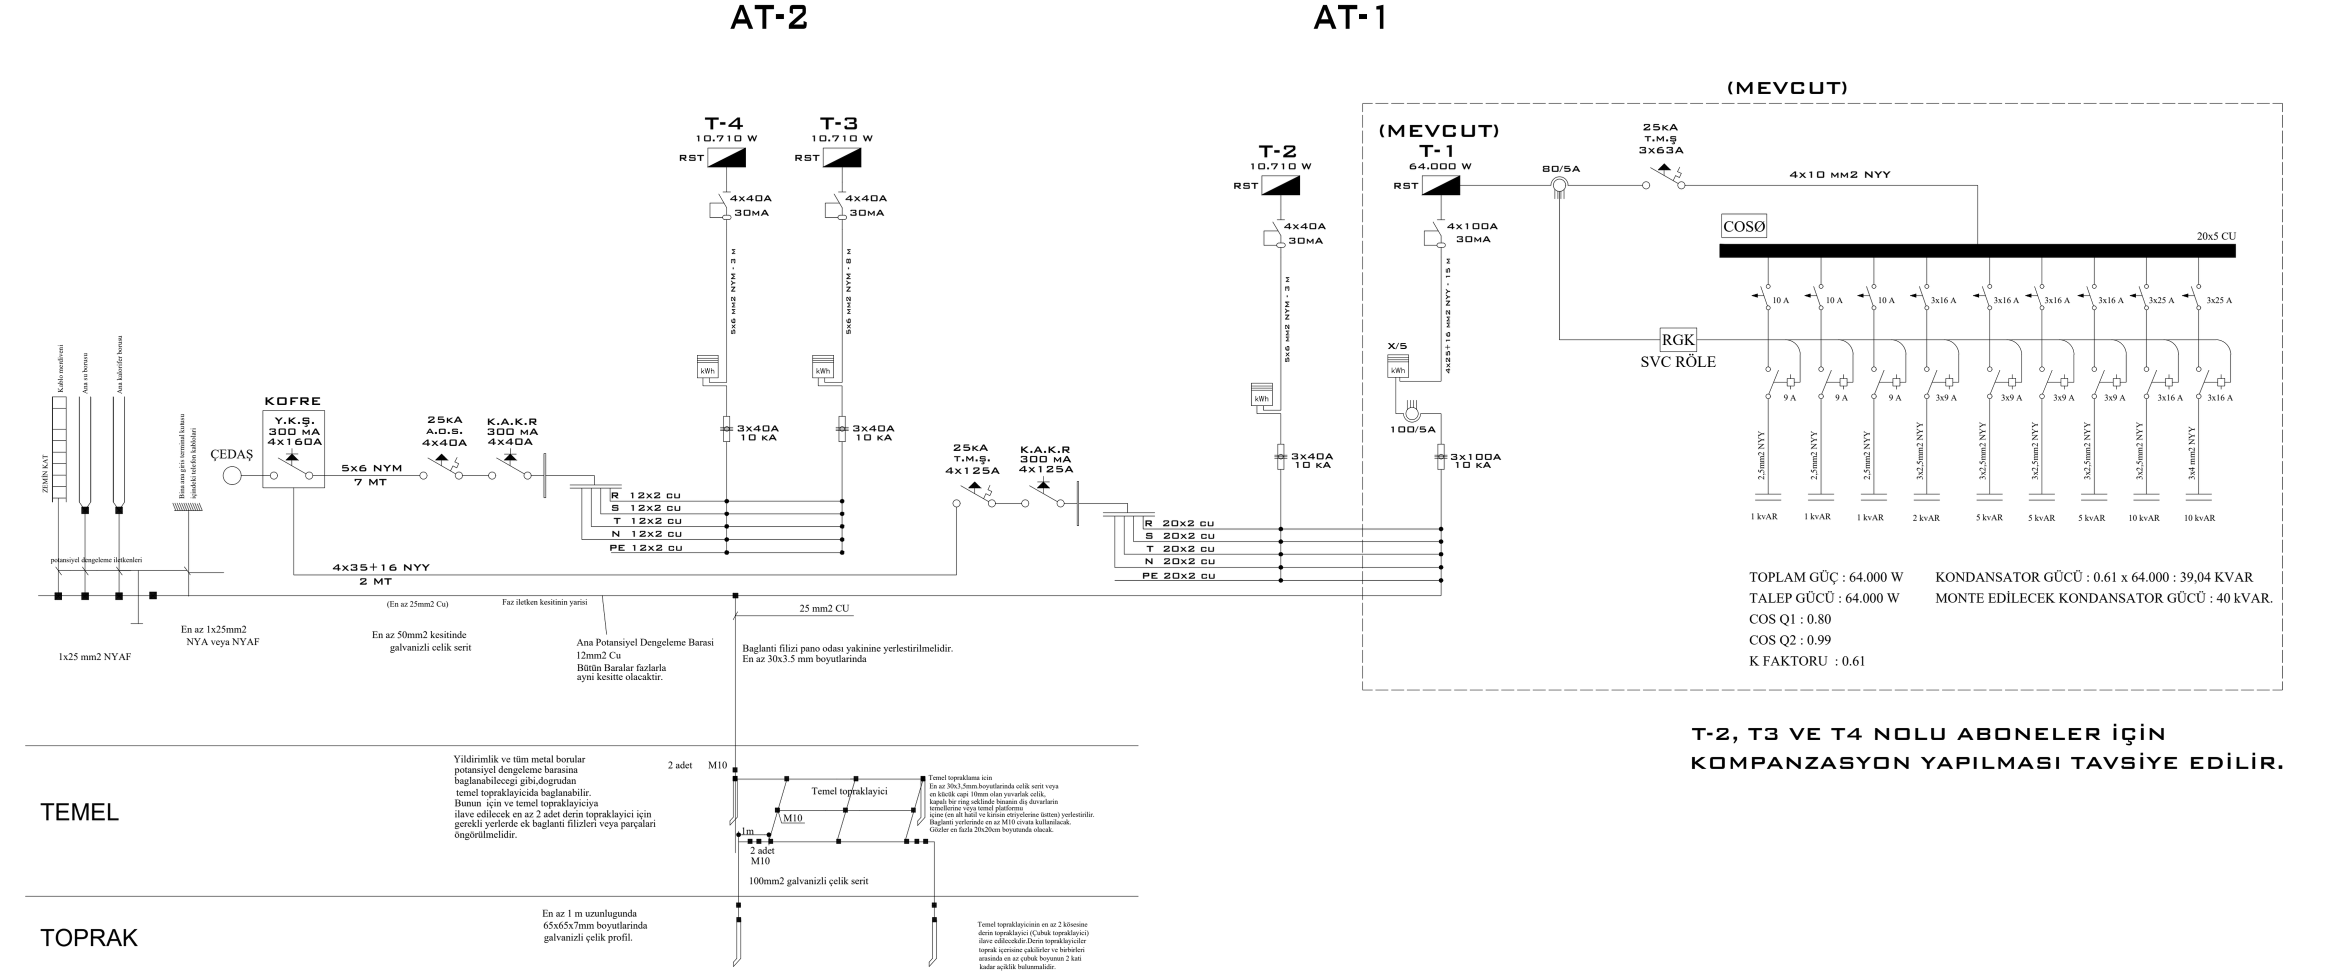


T-2, T3 VE T4 NOLU ABONELER İÇİN KOMPANZASYON YAPILMASI TAVSİYE EDİLİR.

NOT :
Pano gömlek kapakları şeffaf malzemeden yapılacaktır ve mühürlenebilir olmalıdır.

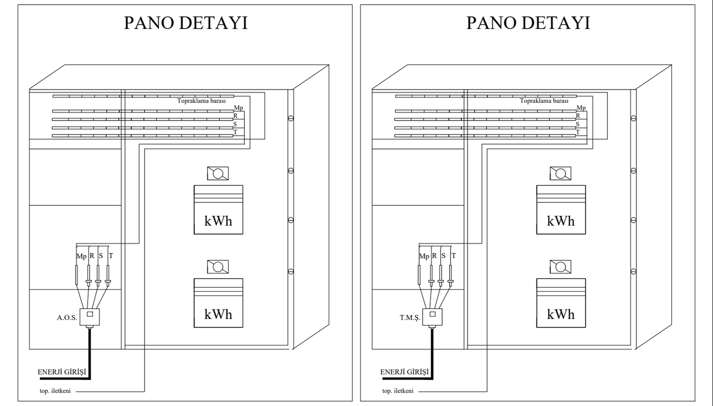


## TEMEL TOPRAKLAMA HESABI

### Derin topraklayıcı

PE = Toprak Özdirenci(ohm.m)
L = Topraklayıcının Uzunluğu (100m)
d = İletkenin Çapı (m)
D = Topraklayıcının çevrelediği alana eşit alanlı çap(m)
A = Topraklayıcının çevrelediği alan (m2)

ÖLÇÜM CİHAZI
MARKA MODEL: ERT-S
SERİ NO:0445382
ÖLÇÜM YÖNTEMİ:4 uçlu karşılaştırma
ÖLÇÜM DEĞERLERİ SONUÇLARI
1.ölçüm 99,4 ohm
2.ölçüm 96,2 ohm
3.ölçüm 98,1 ohm
Toprak özgül direnci ortalaması = 97,9 ohm
RE= PE/2 x L⫪x ln x 4L / d
RE= 97,9/2x3,14x1,5xln x4x1,5/0,02
RE= 97,9/1,652=59,26
Bir kazık için Toprak direnci=59,26 ohm
RE= 59,26 ohm
16A'lik en büyük linye sigortası için 0,4sn'de Zs=1,916 ohm.
1,916>RT olmalıdır.
A=133 m2
D= 1,13 $\sqrt{A}$= 1,13x$\sqrt{133}$ =13,03 m
Rt=(Re/2xD)x(Re/L)/(Re/2xD)+(Re/L)
Rt=(59,26/2x13,03)x(59,26/45)/(59,26/2x13,03)+(59,26/45)
0,834 ohm < 5 ohm olduğundan 4 kazık uygundur.

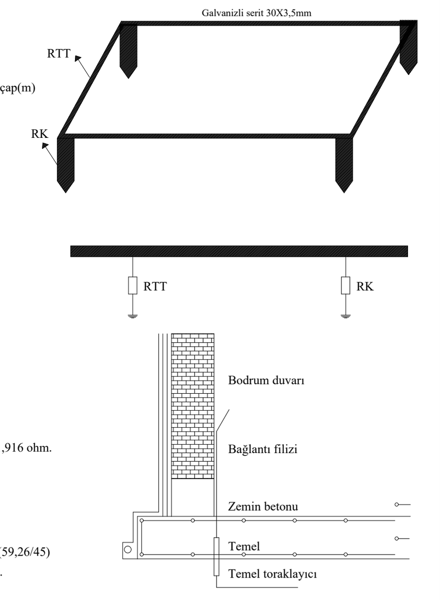


CAN GÜVENLIGINIZ ICIN TOPRAKLAMA YONETMELIGINE MUTLAKA UYUNUZ!
TOPRAKLAMA TESISI 21.08.2001 TARIH VE 24500 SAYILI RESMI GAZETEDE

## SEMBOLLER LİSTESİ

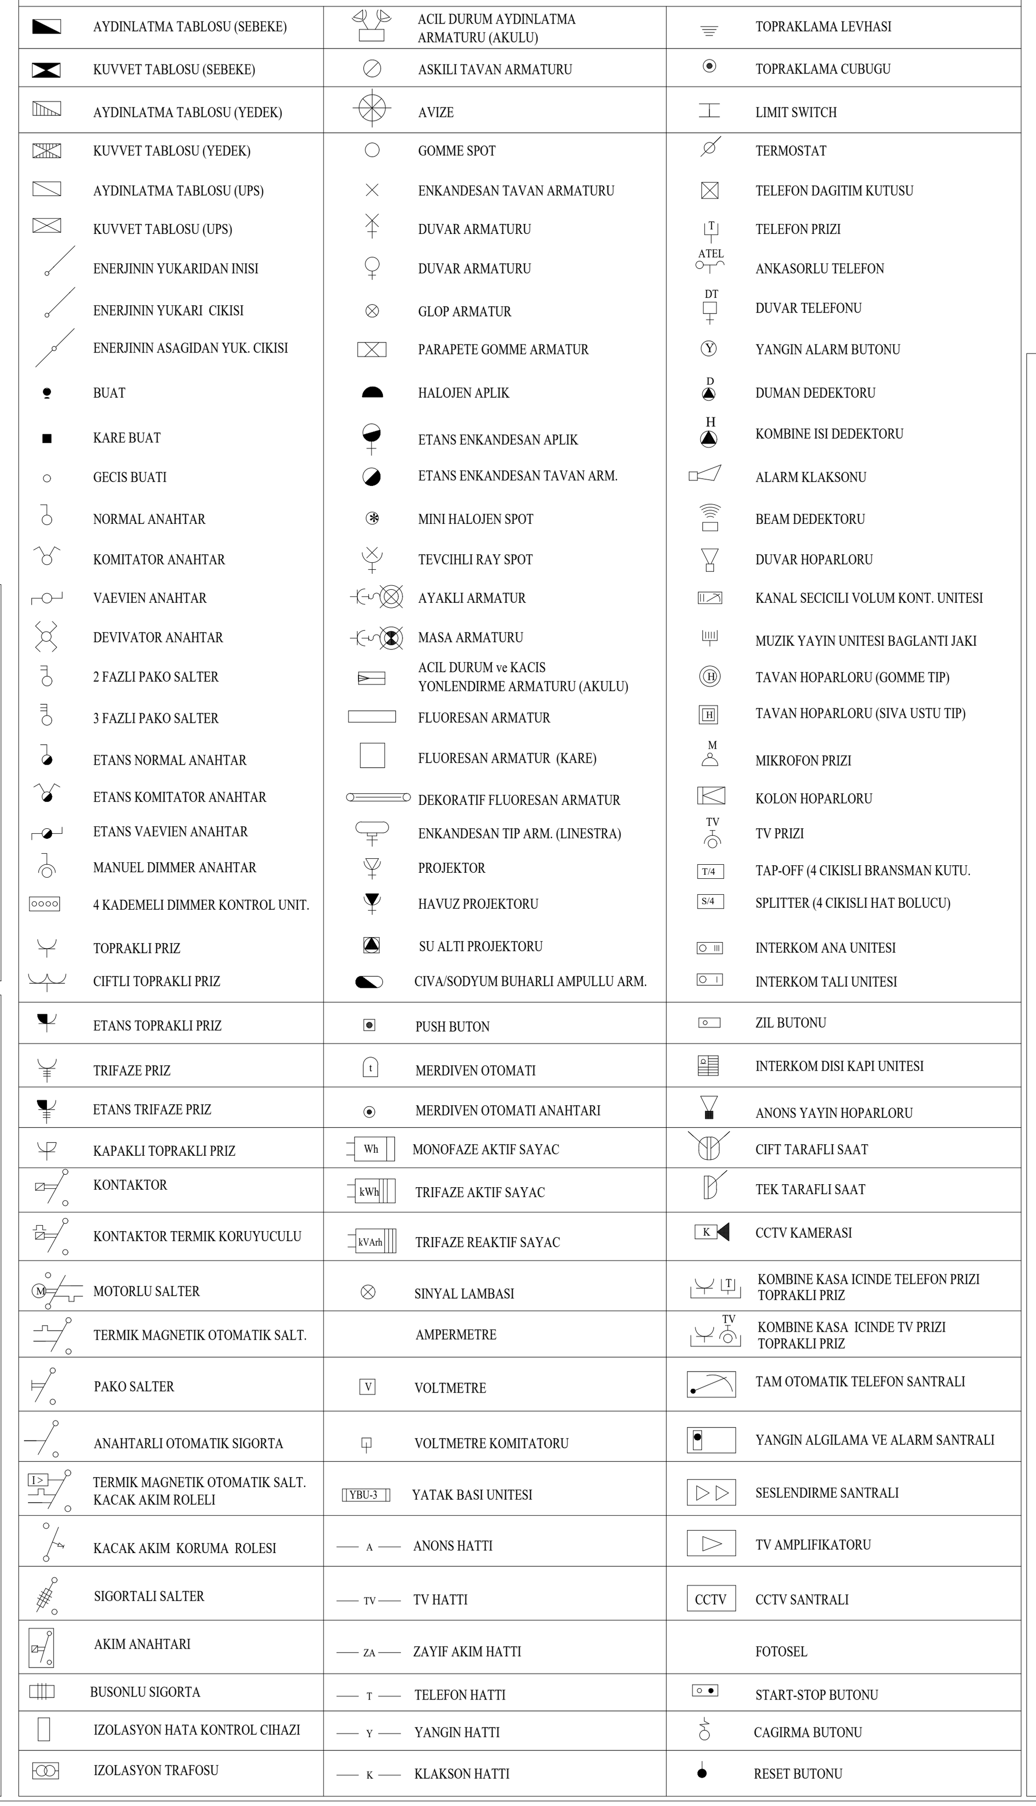


ÖZ ENERJİ MÜHENDİSLİK

## ELEKTRİK İÇ TESİSAT TADİLAT PROJESİ

| PROJE SORUMLUSU | Adı Soyadı | Oda No | SMM No | BT No | Vergi D. | Vergi No | İMZASI |
|---|---|---|---|---|---|---|---|
| | ABDULSAMED ÖZ | 89864 | 06/60-89864 | 06/60-6621086793 | TOKAT | 44683325814 | |

YAPI DENETİM FİRMASI

TÜRK TELEKOM ONAYI

Tarih: No:

ÇEDAŞ SİVAS GENEL MÜDÜRLÜĞÜ

3 YIL MUTEBER OLMAK ÜZERE BELİRTİLDİĞİ ŞEKİLDE TASDİK EDİLMİŞTİR.

| YAPIDA KULLANILACAK SAYAÇ CİNSLERİ VE ADETLERİ | AKTİF ADET | KOMBİ ADET |
|---|---|---|
| Tek Fazlı Sayaç | | |
| Üç Fazlı Direkt Bağlantılı | 3 | |
| Üç Fazlı A.T. Bağlantılı | | 1 |
| Toplam Sayaç Sayısı | 4 | |

YAPIYA AİT ÖZET BİLGİLER

| | | | | | | | |
|---|---|---|---|---|---|---|---|
| YAPI SAHİBİNİN | Adı Soyadı | ALİ UMUT BALCI | | | | | |
| | Adresi | MERKEZ / TOKAT | | | | | |
| | Vergi Dairesi / No | | | | | | |
| YAPININ | İli | TOKAT | İlçe / Belediye | MERKEZ | | | |
| | Adresi | KALEARDI MAHALLESİ | | | | | |
| | Mimari Projesini Onaylayan Kurum | | | Tarih | | Sayı | |
| | Pafta | | Ada | 1245 | Parsel | 2 | |
| | Sınıfı | Toplam Kat Sayısı | 2 | Toplam Alan ( m² ) | | | |
| | Süresi (Ay) | Bağımsız Bölüm Sayısı | 4 | Kullanım Amacı | TİCARETHANE | | |

PROJEYE AİT ÖZET GÜÇ BİLGİLERİ

| GÜÇ BİLGİLERİ | | | | |
|---|---|---|---|---|
| | Toplam Kurulu Gücü (W) | 64.000 | Yeni Eklenen Güç (W) | 32.130 |
| | Eşzamanlılık Faktörü (%) | %100 | Yeni Toplam Kurulu Güç (W) | 96.130 |
| | Eşzamanlı Güç (W) | 64.000 | Yeni Eşzamanlı Güç (W) | 96.130 |

| PRO. ÇİZEN | ÇİZİM TARİHİ | ÖLÇEK | PROJE NO |
|---|---|---|---|
| Abdulsamed ÖZ | 05.02.2026 | 1/50 | |

E

Tesisat muayeneleri esnasında kullanılacak olan proje müeesesede kaşelenen arşiv kaşeli projedir.
Üzerinde silinti, kazıntı veya onaysız tadilat görmüş projeler geçersizdir.
Mimari ile gerçekleşen fiziki yapı birbirinin aynısı değilse proje geçersizdir.