


YAPI APLİKASYON PROJESİ

KOORDİNE ÖZET ITRF

NoktaNo	Y	X	M.K	NoktaNo	Y	X	M.K
1	573670.07	4083325.92		B23	573640.82	4083267.01	0.09
2	573675.88	4083321.53		B24	573636.41	4083319.26	
3	573691.21	4083231.41		B25	573654.92	4083321.26	
15	573626.89	4083321.24		B26	573655.29	4083318.99	
16	573642.17	4083226.10		B27	573662.55	4083319.88	
A1	573636.92	4083316.07	0.09	B28	573662.91	4083317.60	
A2	573644.76	4083317.32	0.09	B29	573673.22	4083319.26	
A3	573651.32	4083276.45	0.09	B30	573674.06	4083314.34	
A4	573652.14	4083275.73	0.09	B31	573669.02	4083313.52	
A5	573648.79	4083271.82	0.09	B32	573669.61	4083309.85	
A6	573646.90	4083273.44	0.09	B34	573660.31	4083308.35	
A7	573645.76	4083272.11	0.09	B35	573664.34	4083283.26	
A8	573639.38	4083271.09	0.09	B36	573681.91	4083268.20	
A9	573638.46	4083276.81	0.09	B37	573685.03	4083249.87	
A10	573639.55	4083276.99	0.09	B38	573682.03	4083246.37	
A11	573639.27	4083278.72	0.09	B39	573683.74	4083244.90	
A12	573638.25	4083278.55	0.09	B40	573675.25	4083235.00	
A13	573637.62	4083282.48	0.09	B41	573673.53	4083236.47	
A14	573638.10	4083282.56	0.09	B42	573673.28	4083236.18	
A15	573637.35	4083287.20	0.09	B43	573641.38	4083263.54	
A16	573639.77	4083287.59	0.09	B44	573637.39	4083286.95	
A17	573639.38	4083290.03	0.09	B45	573637.19	4083286.92	
A18	573639.67	4083290.07	0.09	B46	573636.00	4083294.36	
A19	573639.61	4083290.47	0.09	B47	573636.10	4083294.38	
A20	573638.53	4083290.29	0.09	B48	573635.30	4083299.40	
A21	573638.30	4083291.68	0.09	B49	573635.56	4083299.44	
A22	573638.70	4083291.74	0.09	B50	573633.98	4083309.26	
A23	573638.46	4083293.22	0.09	B51	573636.53	4083309.67	
A24	573639.15	4083293.33	0.09	B52	573637.69	4083311.28	
A25	573638.95	4083294.59	0.09	F1	573630.06	4083320.44	
A26	573636.19	4083294.14	0.09	F2	573632.77	4083320.88	
A27	573635.34	4083299.40	0.09	F3	573634.48	4083310.26	
A28	573638.11	4083299.85	0.09	F4	573631.76	4083309.83	
A29	573636.30	4083311.06	0.09	F5	573676.29	4083292.31	
A30	573636.90	4083311.15	0.09	F6	573679.74	4083292.89	
A31	573636.53	4083313.47	0.09	F7	573682.14	4083278.80	
A32	573637.32	4083313.60	0.09	F8	573678.69	4083278.21	
B1	573640.16	4083271.16	0.09	G1	573669.34	4083320.67	
B2	573645.78	4083272.06	0.09	G2	573673.29	4083321.30	
B3	573646.90	4083273.37	0.09	G3	573673.61	4083319.33	
B4	573651.18	4083269.70	0.09	G4	573669.66	4083318.69	
B5	573653.97	4083272.96	0.09	H1	573662.16	4083307.89	0.09
B6	573683.11	4083247.94	0.09	H2	573667.06	4083308.67	0.09
B7	573683.15	4083247.68	0.09	H3	573667.98	4083308.24	0.09
B8	573678.22	4083241.93	0.09	H4	573668.14	4083307.84	0.09
B9	573676.09	4083243.75	0.09	H5	573671.45	4083287.24	0.09
B10	573675.31	4083242.84	0.09	H6	573676.85	4083282.59	0.09
B11	573677.44	4083241.02	0.09	H7	573677.06	4083281.82	0.09
B12	573672.39	4083235.14	0.09	H8	573676.83	4083281.31	0.09
B13	573657.67	4083247.78	0.09	H9	573673.60	4083277.55	0.09
B14	573658.83	4083249.12	0.09	H10	573672.86	4083277.24	0.09
B15	573656.54	4083251.08	0.09	H11	573672.23	4083277.49	0.09
B16	573655.38	4083249.74	0.09	H12	573665.04	4083283.65	0.09
B17	573640.67	4083262.37	0.09	H13	573661.33	4083306.74	0.09
B18	573641.20	4083262.99	0.09	H14	573661.46	4083307.41	0.09
B19	573640.59	4083263.51	0.09	H15	573643.33	4083247.31	0.09
B20	573641.90	4083265.03	0.09	H16	573643.46	4083247.64	0.09
B21	573640.69	4083266.07	0.09	H17	573644.15	4083247.68	0.09
B22	573641.21	4083266.68	0.09	H18	573660.74	4083233.45	0.09
				H19	573660.88	4083233.04	0.09
				H20	573660.44	4083232.61	0.09
				H21	573651.49	4083231.64	0.09
				H22	573644.93	4083237.26	0.09
				H23	573676.62	4083280.68	0.09
				H24	573677.06	4083280.81	0.09
				H25	573677.33	4083280.53	0.09
				H26	573678.56	4083273.25	0.09
				H27	573678.32	4083272.77	0.09
				H28	573677.71	4083272.79	0.09
				H29	573673.62	4083276.30	0.09
				H30	573673.48	4083276.68	0.09
				H31	573673.59	4083277.15	0.09
				K1	573652.14	4083318.64	
				K2	573657.08	4083319.44	
				K3	573658.37	4083311.53	
				K4	573653.42	4083310.72	
				M1	573640.50	4083236.50	
				M2	573643.36	4083236.95	
				M3	573644.04	4083236.25	
				M4	573645.02	4083237.19	
				M5	573651.70	4083231.66	
				M6	573647.48	4083226.68	
				M7	573668.96	4083302.76	
				M8	573673.67	4083303.51	
				M9	573677.03	4083283.77	
				M10	573675.74	4083283.56	

ALAN HESABI (ITRF96-2005E)

ADA	PARSEL	ALAN (m²)	KAT ADEDİ
15483	2	4.692,05	
	A BLOK	478.12	7
	B BLOK	714.31	7

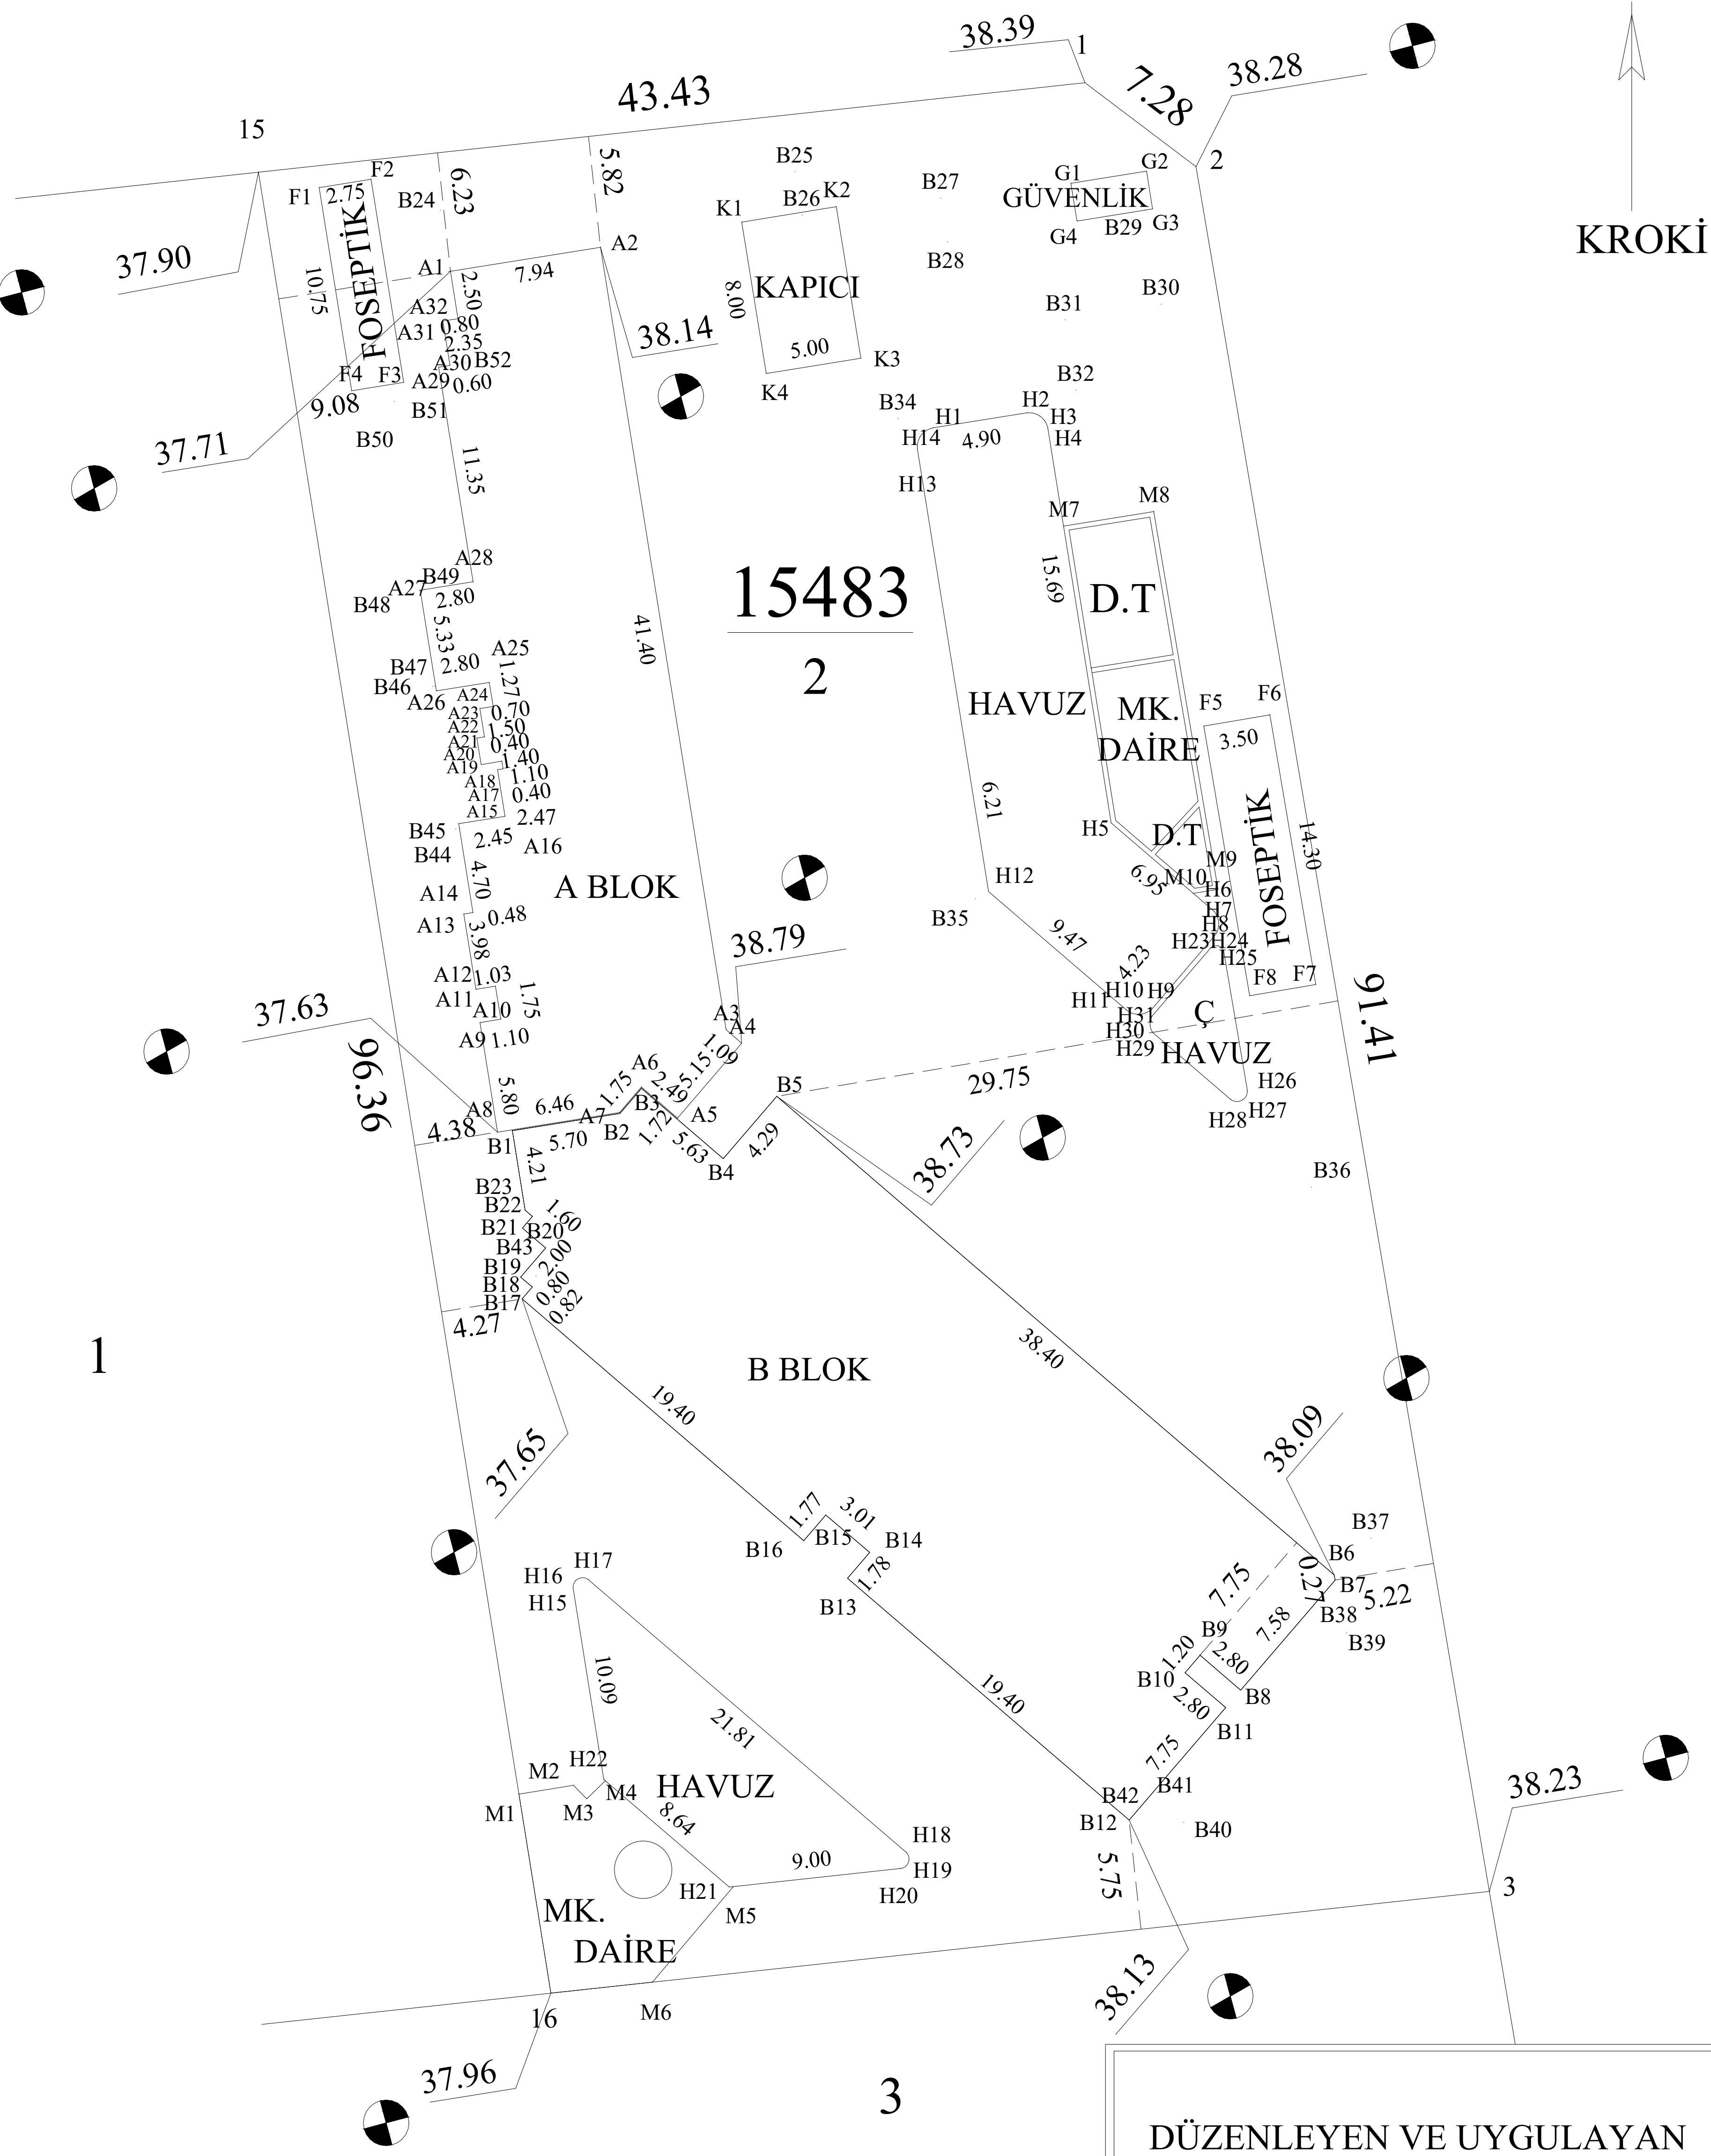

DÜZENLEYEN VE UYGULAYAN
HARİTA MÜHENDİSİ

ADI SOYADI

TARİH

İMZA

DENETİME İLİŞKİN
FENNİ MESUL / İDARE
HARİTA MÜHENDİSİ

ONAY (MÜHÜR)
İDARE

... / /

... / ... /

İLİ	ANTALYA
İLÇESİ	AKSU
MAH/KÖY	ALTINTAŞ
PAFTA	O25-B-12-B-4-D
ADA	15483
PARSEL	2

Proje Koordinat Bilgisi:

Datum : ITRF96(GRS80)

Projeksiyon : UTM 3

Elipsoid :

D.O.M. : 30

Dilim : 3

Referans Yükseklik :Ortometrik

Dönüşüm Bilgisi

MEGSIS Dönüşüm ID :

Lejant :

⊗ : Parsel Zemin Kotu

⊙ : Bina Zemin Kotu

Açıklamalar :